EMMA LEHTINEN

PORTFOLIO 2017-2020

Innehållförteckning

1. CV sida 1
2. Smygehuk sida 2-5
3. Blomsterkioksen sida 6-11
4. Varvsstaden sida 12 -19
5. The private one sida 20-22
6. Sege park sida 23-26
7. Södra verket sida 27-33

CV

UTBILDNING

Filbornaskolan, Helsingborg
- Pedagogprogrammet
Augusti 2008 - Juni 2011

Malmö Universitet
- Internationella relationer
September 2012 - Juni 2013

Linnéuniversitetet
- Ämneslärare inrkt historia
September 2014- Juni 2016

Malmö Universitet
– Arkitektur, visualisering, kommunikation
September 2017- Juni 2020

MALMÖ UNIVERSITET
- Urban studies
September 2021 - Juni 2023

PROGRAMKUNSKAPER

Adobe Illustrator CC 2018
Adobe Indesign CC 2018
Adobe Photoshop CC 2018
3DS Max
AutoCAD
Sketch Up

ARBETSLIVSERFARENHET

OJ ICA KVANTUM, Helsingborg
– Kassörska
Juni 2011- April 2016

Vikare på Magnusstenbocksskolan
- Barnskötare
Höstterminen 2012

Helsingborgs Idrottsförening
- Volontär
April 2010- juli 2014

Scandlines, Drive in
- Kassörska
Sommaren 2017

Coop Stenbooksgatan, Helsingborg
- Kassörska
Maj 2018- Juli 2023



2 Smygehuk

POSTER



- TRE UPPGIFTER SOM SYFTEDE PÅ ATT GE KUNSKAP I BILDKOMPOSITION OCH GRUNDLÄGGANDE BILDBEHANDLING, SKAPA EN LOGGA TILL PLATSEN MED TILLHÖRANDE TYPSNITT I FORM AV EN VEKTORISERAD TYPOGRAFISK BILD. SKAPA EN POSTER OCH EN FLYER FÖR ETT FIKTIVT EVENT PÅ PLATSEN

KOM OCH FIRA
SVERIGES NATIONALDAG PÅ
KÖPMANSGÅRDEN
SMYGEHUK



WORKSHOPS

TEMA: KERAMIK

BARN ÅR 5-15
VUXNA
PENSIONÄR

KVÄLLEN: Picknick
1 korg för 150kr
2 korgar för 230kr


FRAMSIDA

Besök oss på plats

Köpmansgården, Smygehuk.
Smyge strandväg 4 c, 231 78 Smygehamn
Telefon: 0410-73 33 20

På webben kan du besöka oss på:
www.KGarden.se
Instagram: KGarden
Facebook: www.facebook.se/KGarden

Kollektivtrafik:
Ta pågatåget till **Trelleborg C** och regionbuss **190 mot Ystad.**
Hållplats, Smyehuk hamn.

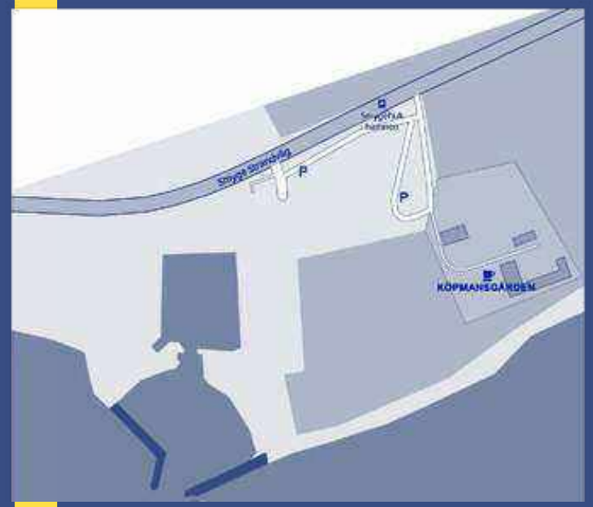

KÖPMANSGÅRDEN Smygehuk

BAKSIDA

LOGGOTYP



ALTERNATIV 1





ALTERNATIV 2



3 Blomsterkiosk

Fasader

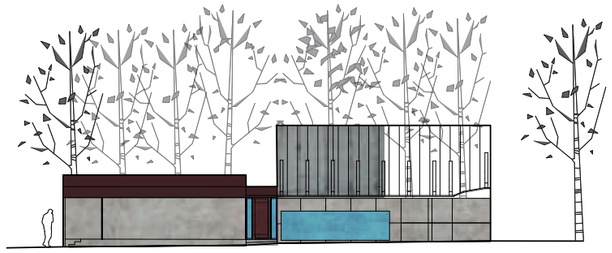

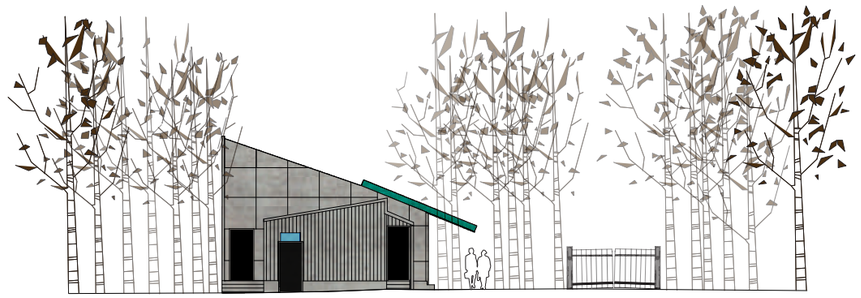




- ta fram ett grafiskt material som beskriver Lewerentz blomsterkiosk, dess versamhet och relation till Östra kyrkogården. Materialet skall fånga och representera de arkitektoniska värden som byggnaden och platsen besitter. Jag gjorde om fasader och sektion. Skapade egen situationsplan. Jag använde mig av skalorna, 1:100 och 1:200. Vidare använde jag mig av att fotografera platsen och byggnaden. Jag skapade interiöra och extriöra bilder i photosop och avslutade med att samla allt arbete i en poster.







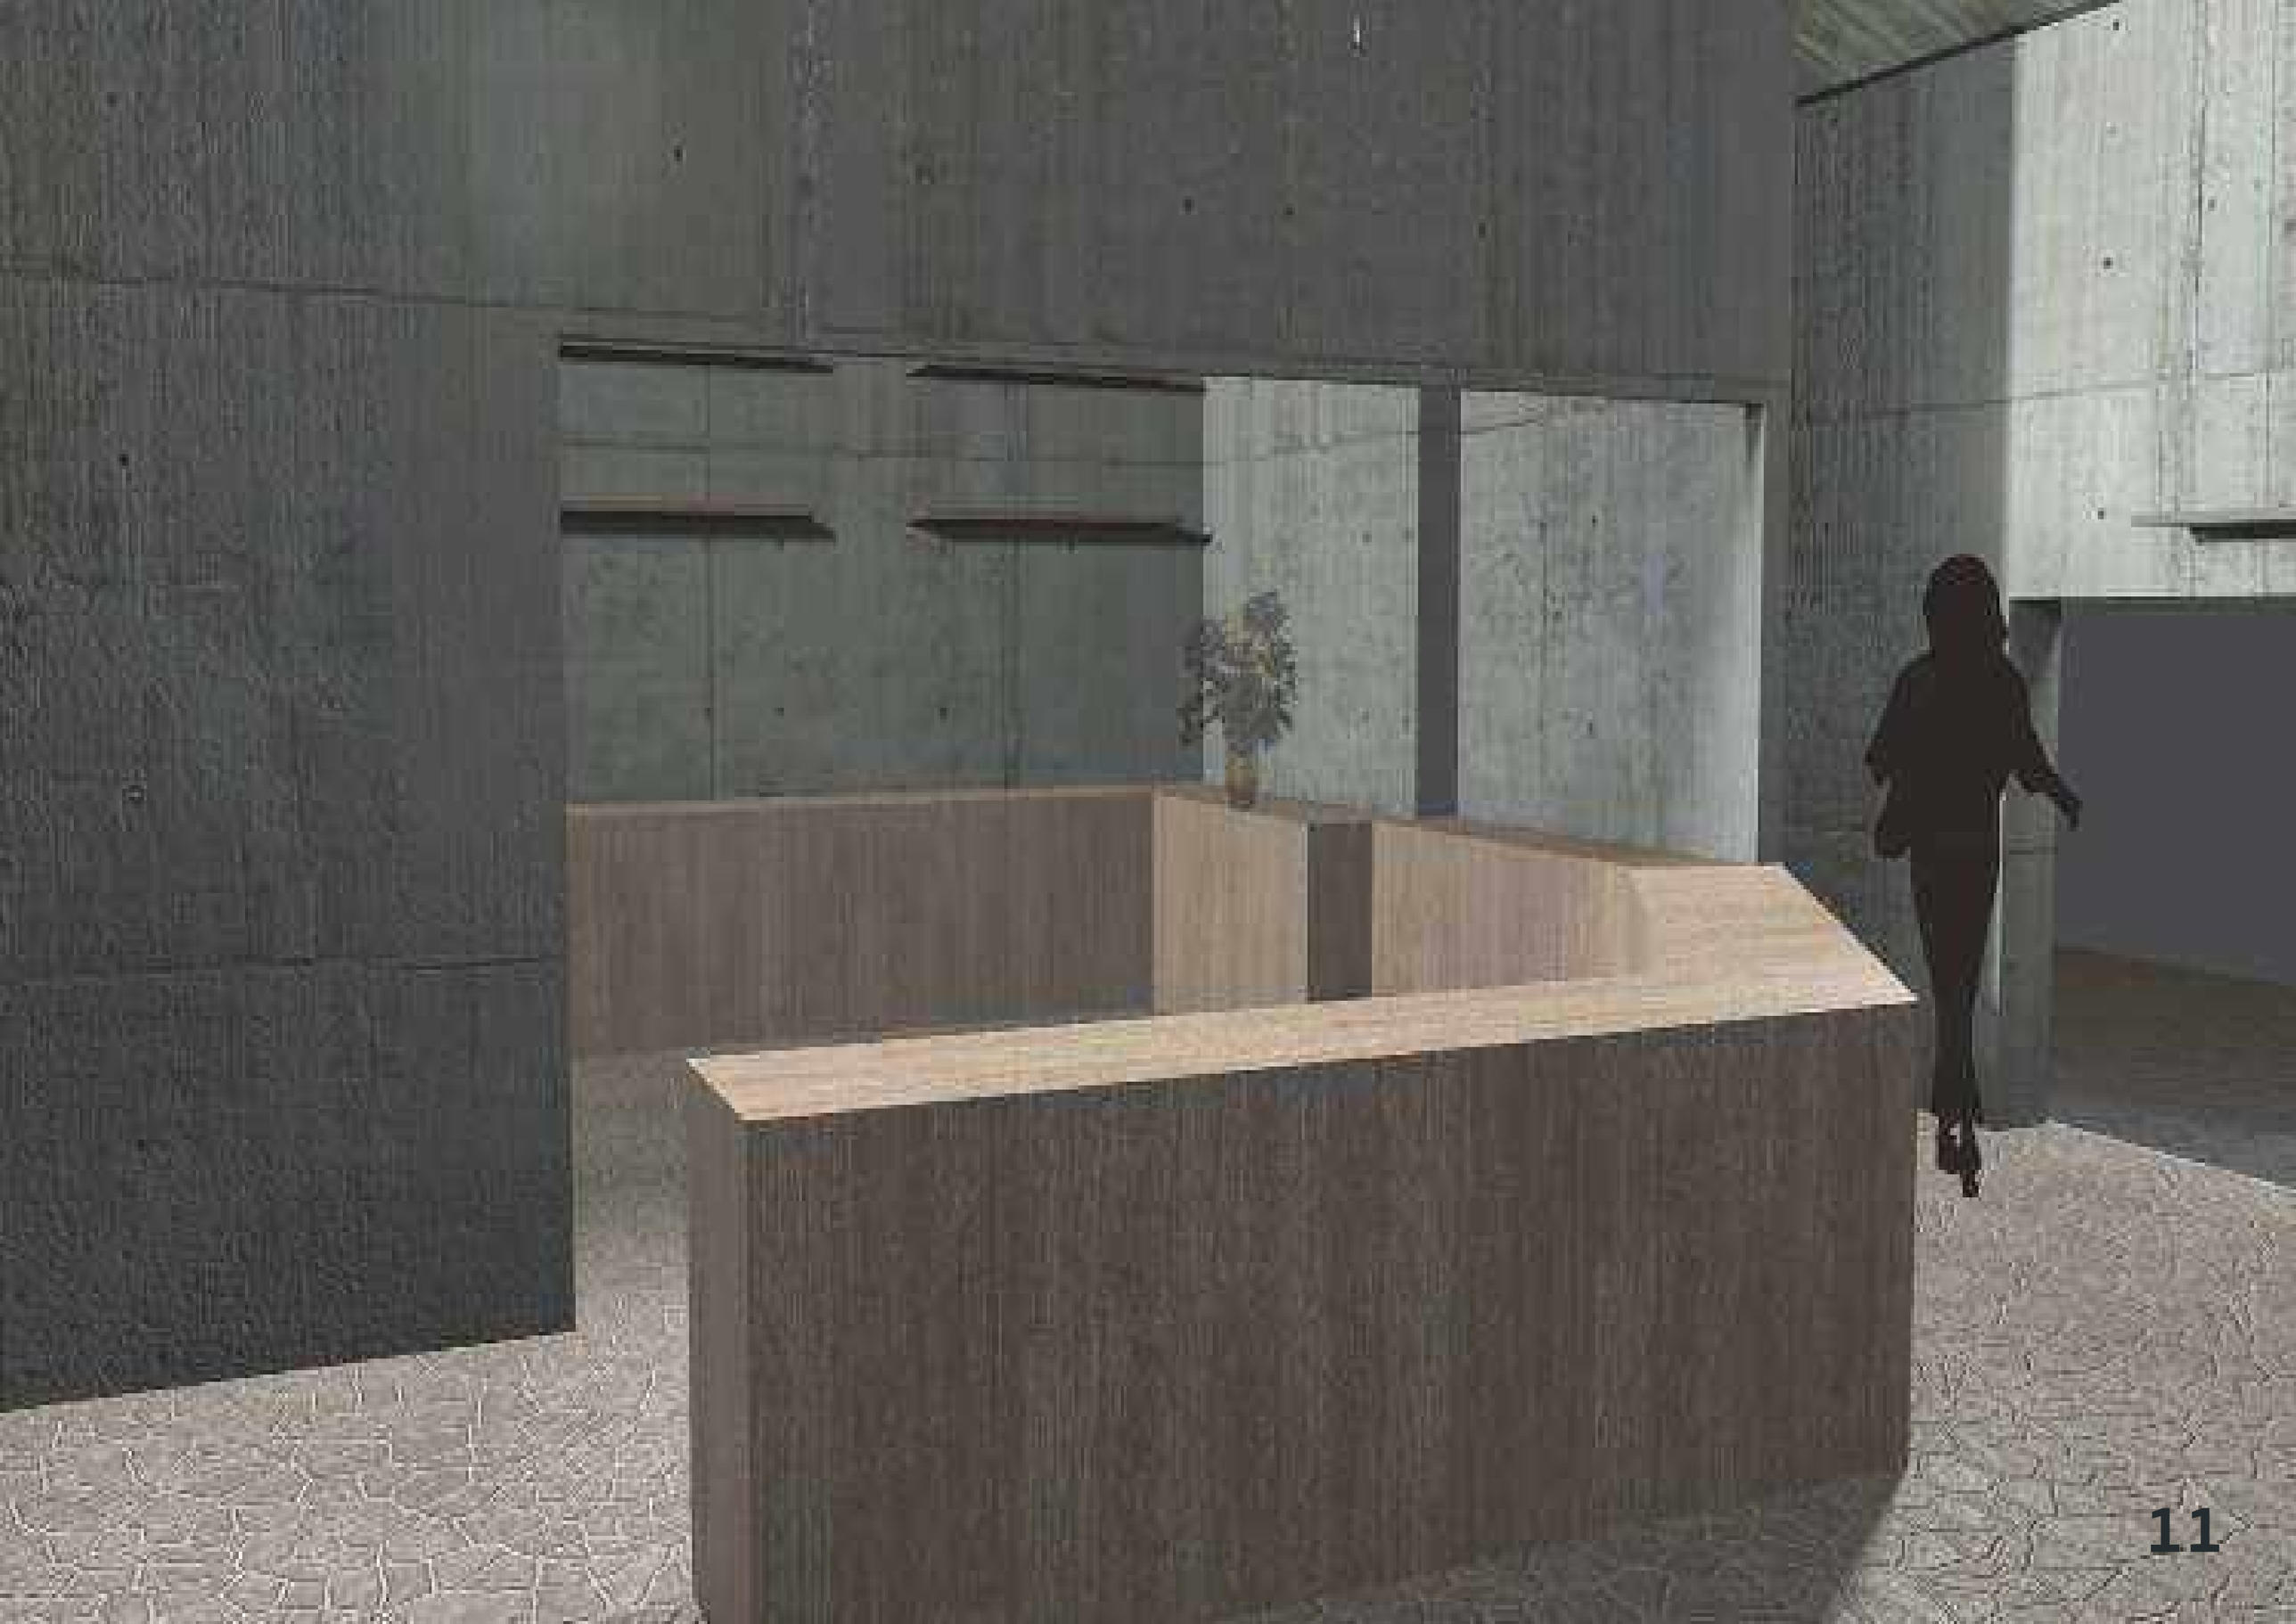




4 VARVSSTADEN

3D-MAX

- Modelleringsövning till grundläggande modelleringstekniker och skapa korrekta och skalenliga 3d-modeller av de tre små byggnader. Med hjälp vraymaterial ska byggnaden materialsättas, kameramatchning och bildbehandlingsövning. Slutuppggiften gick ut på att ta fram ett presentationsmaterial för den byggnad jag valt ut och den plats som skapats i anslutning till Varvsstaden.


[+] [Perspective] [High Quality] [Edged Faces]



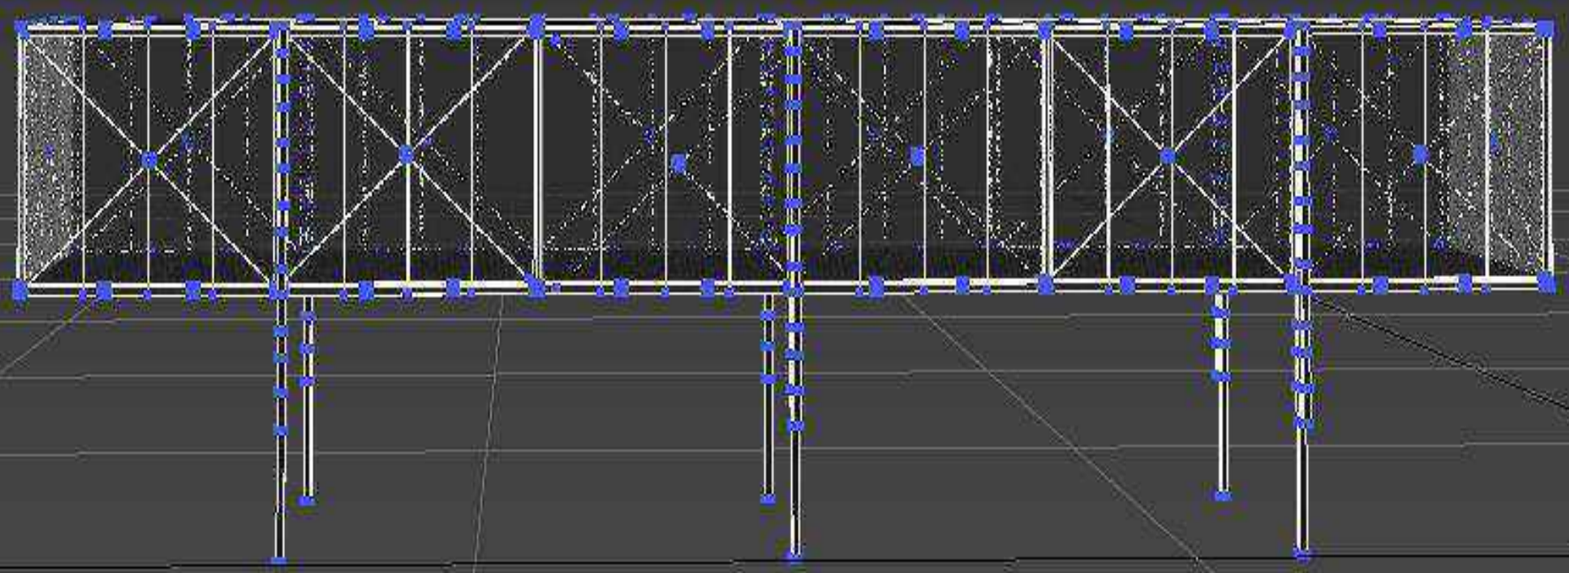



[+][Perspective][Standard][Edged Faces]



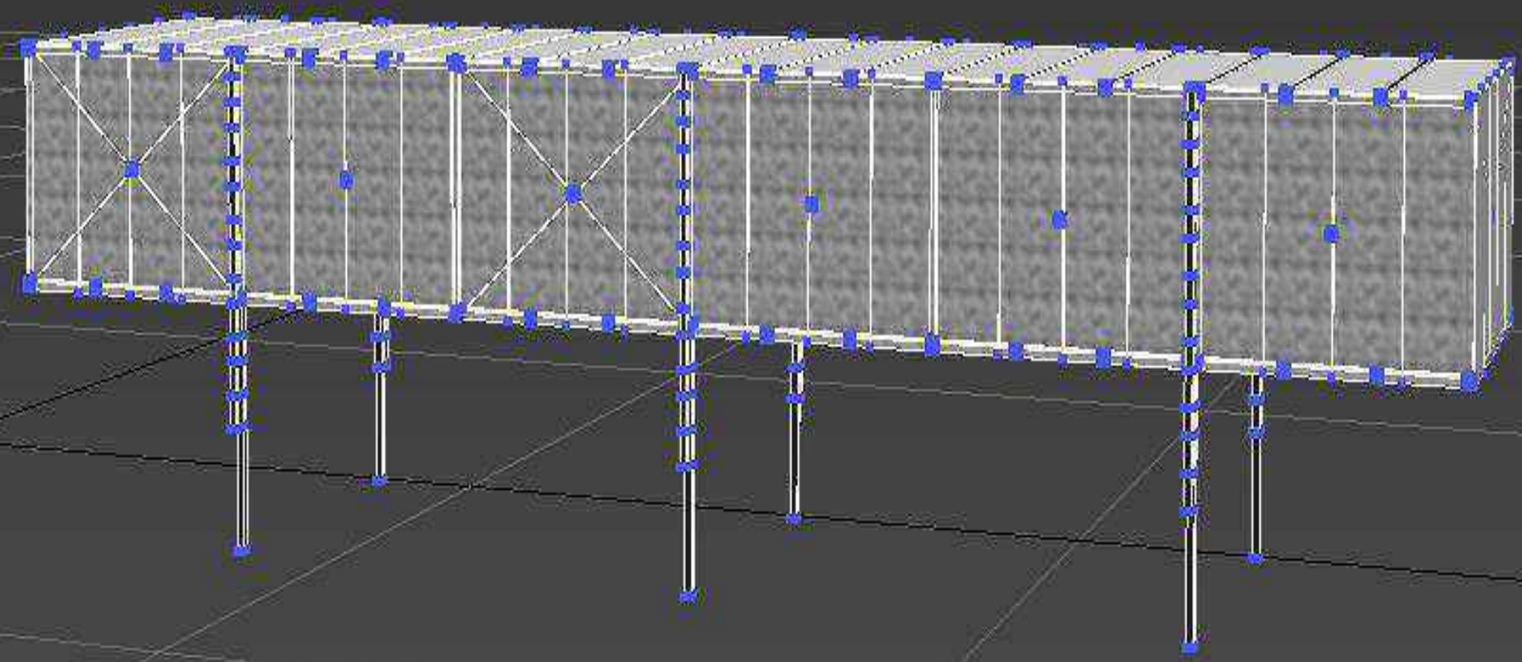



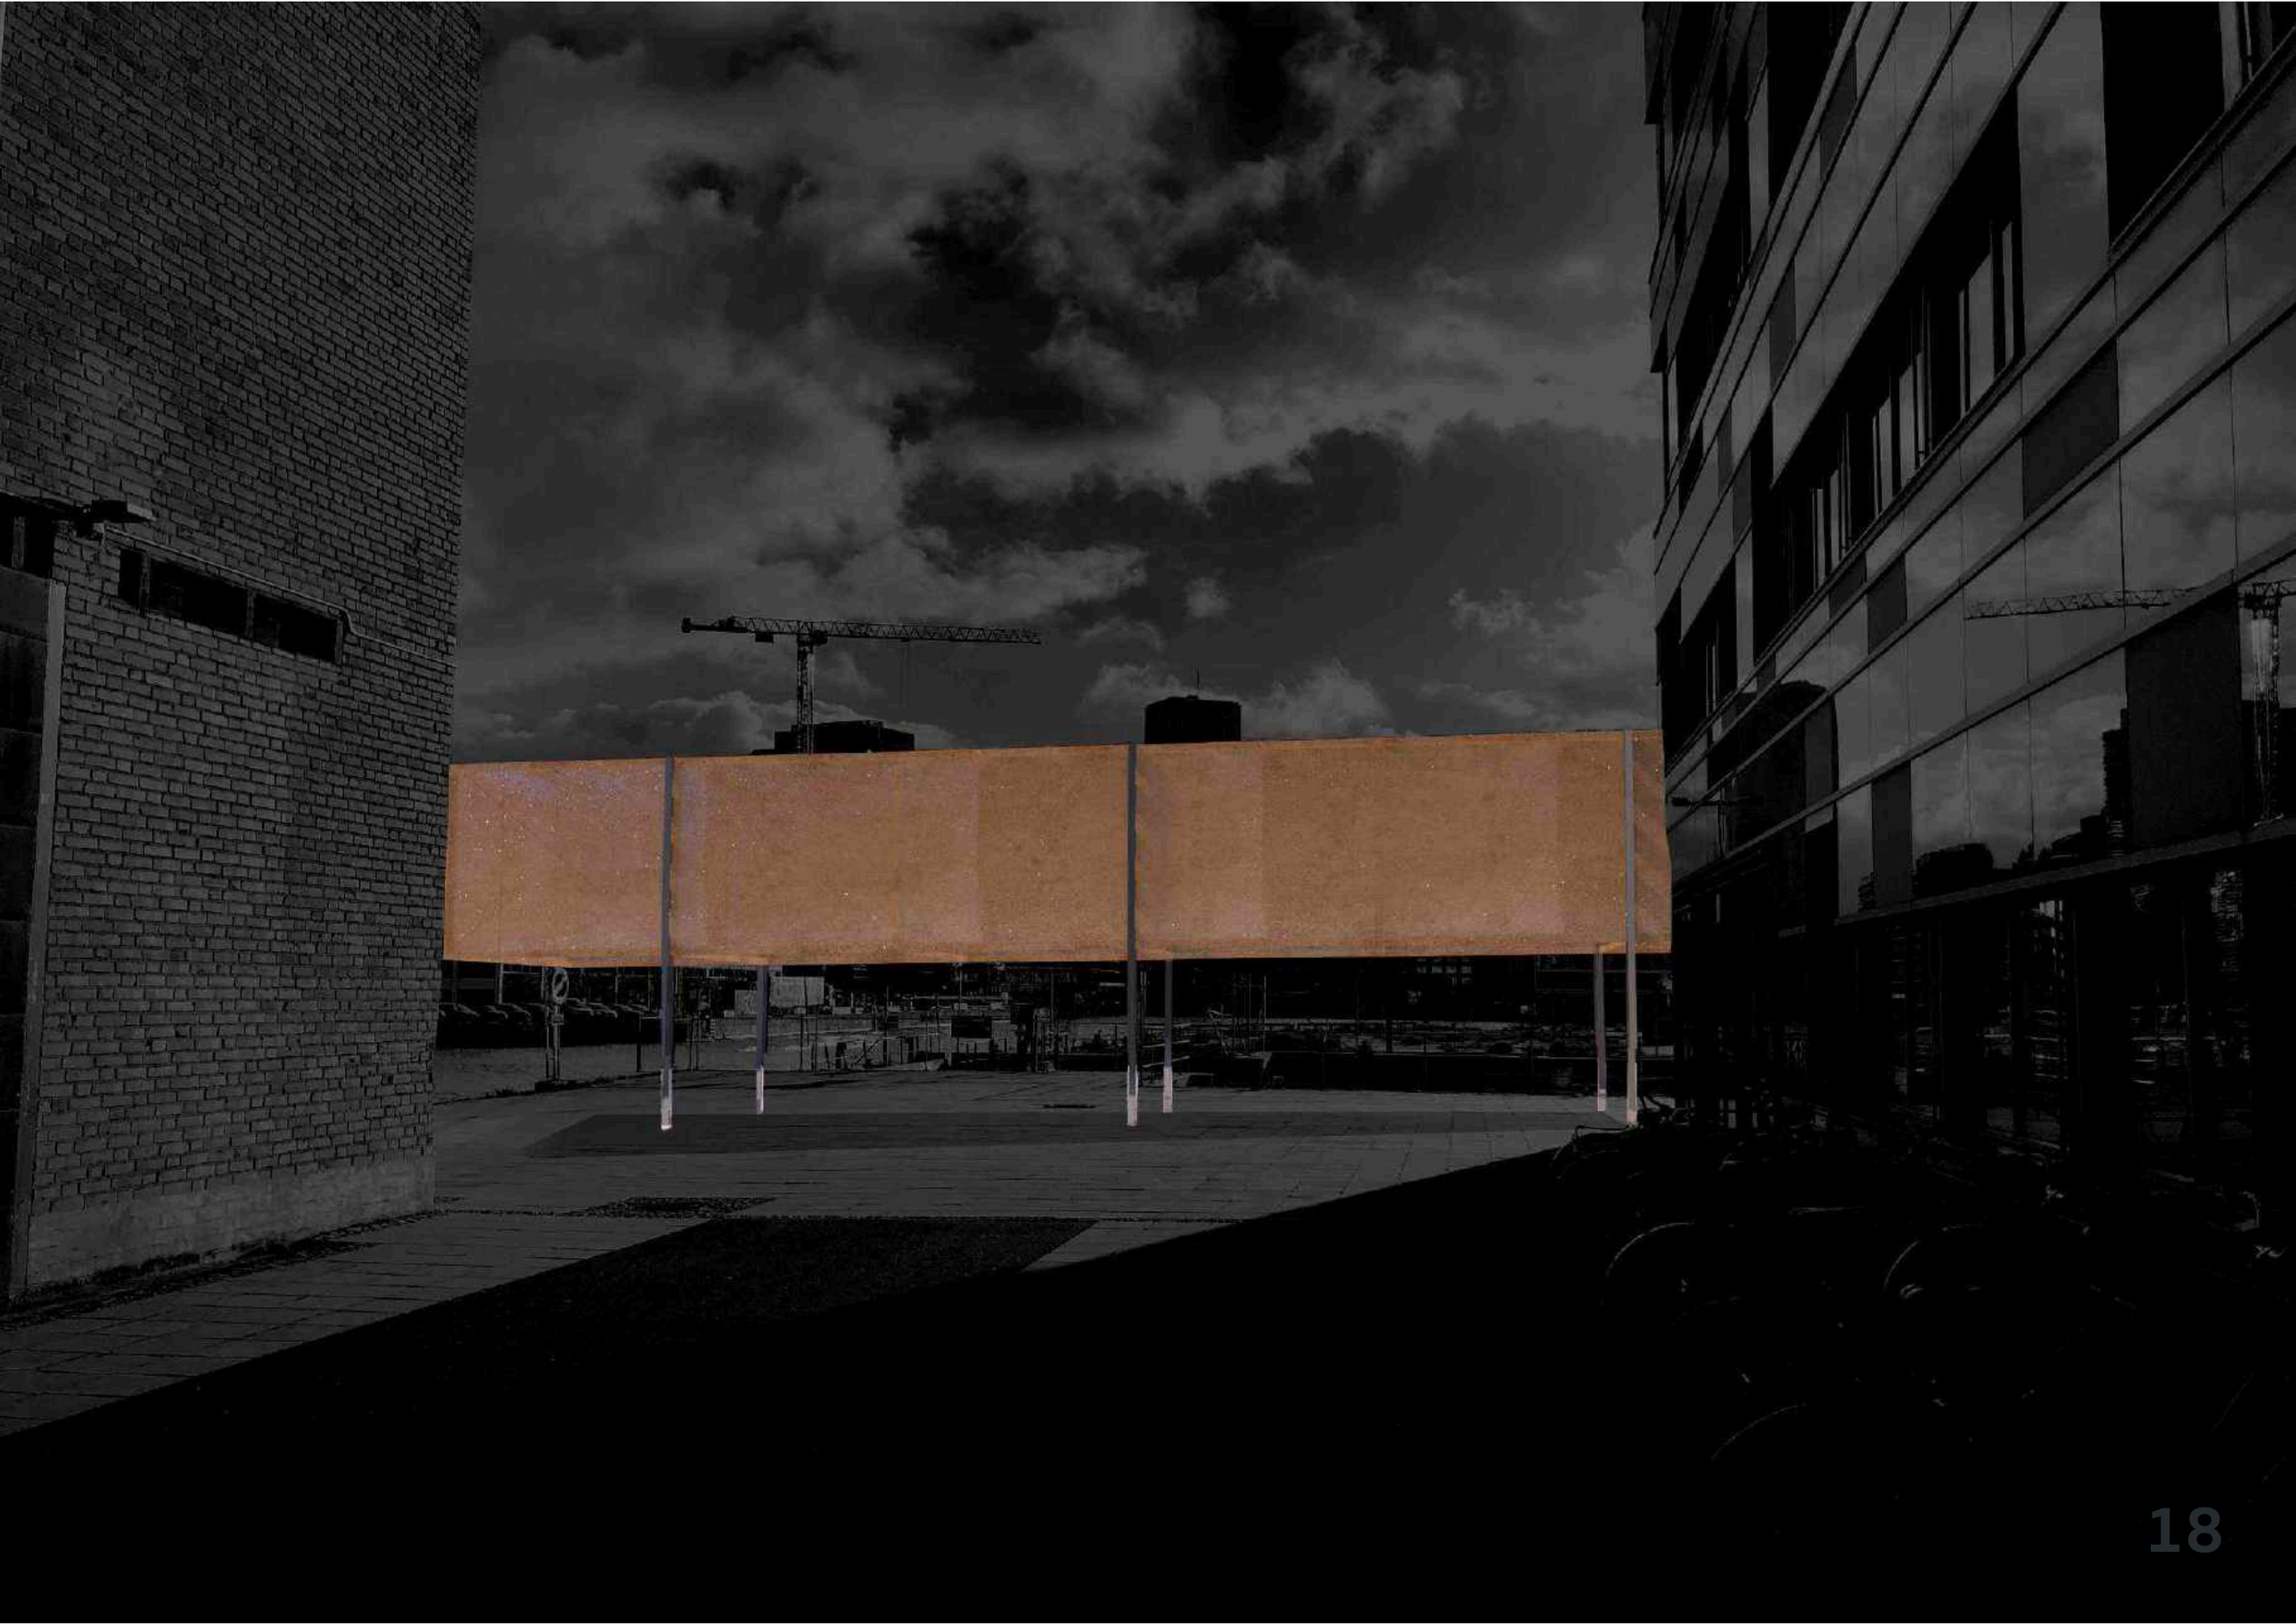


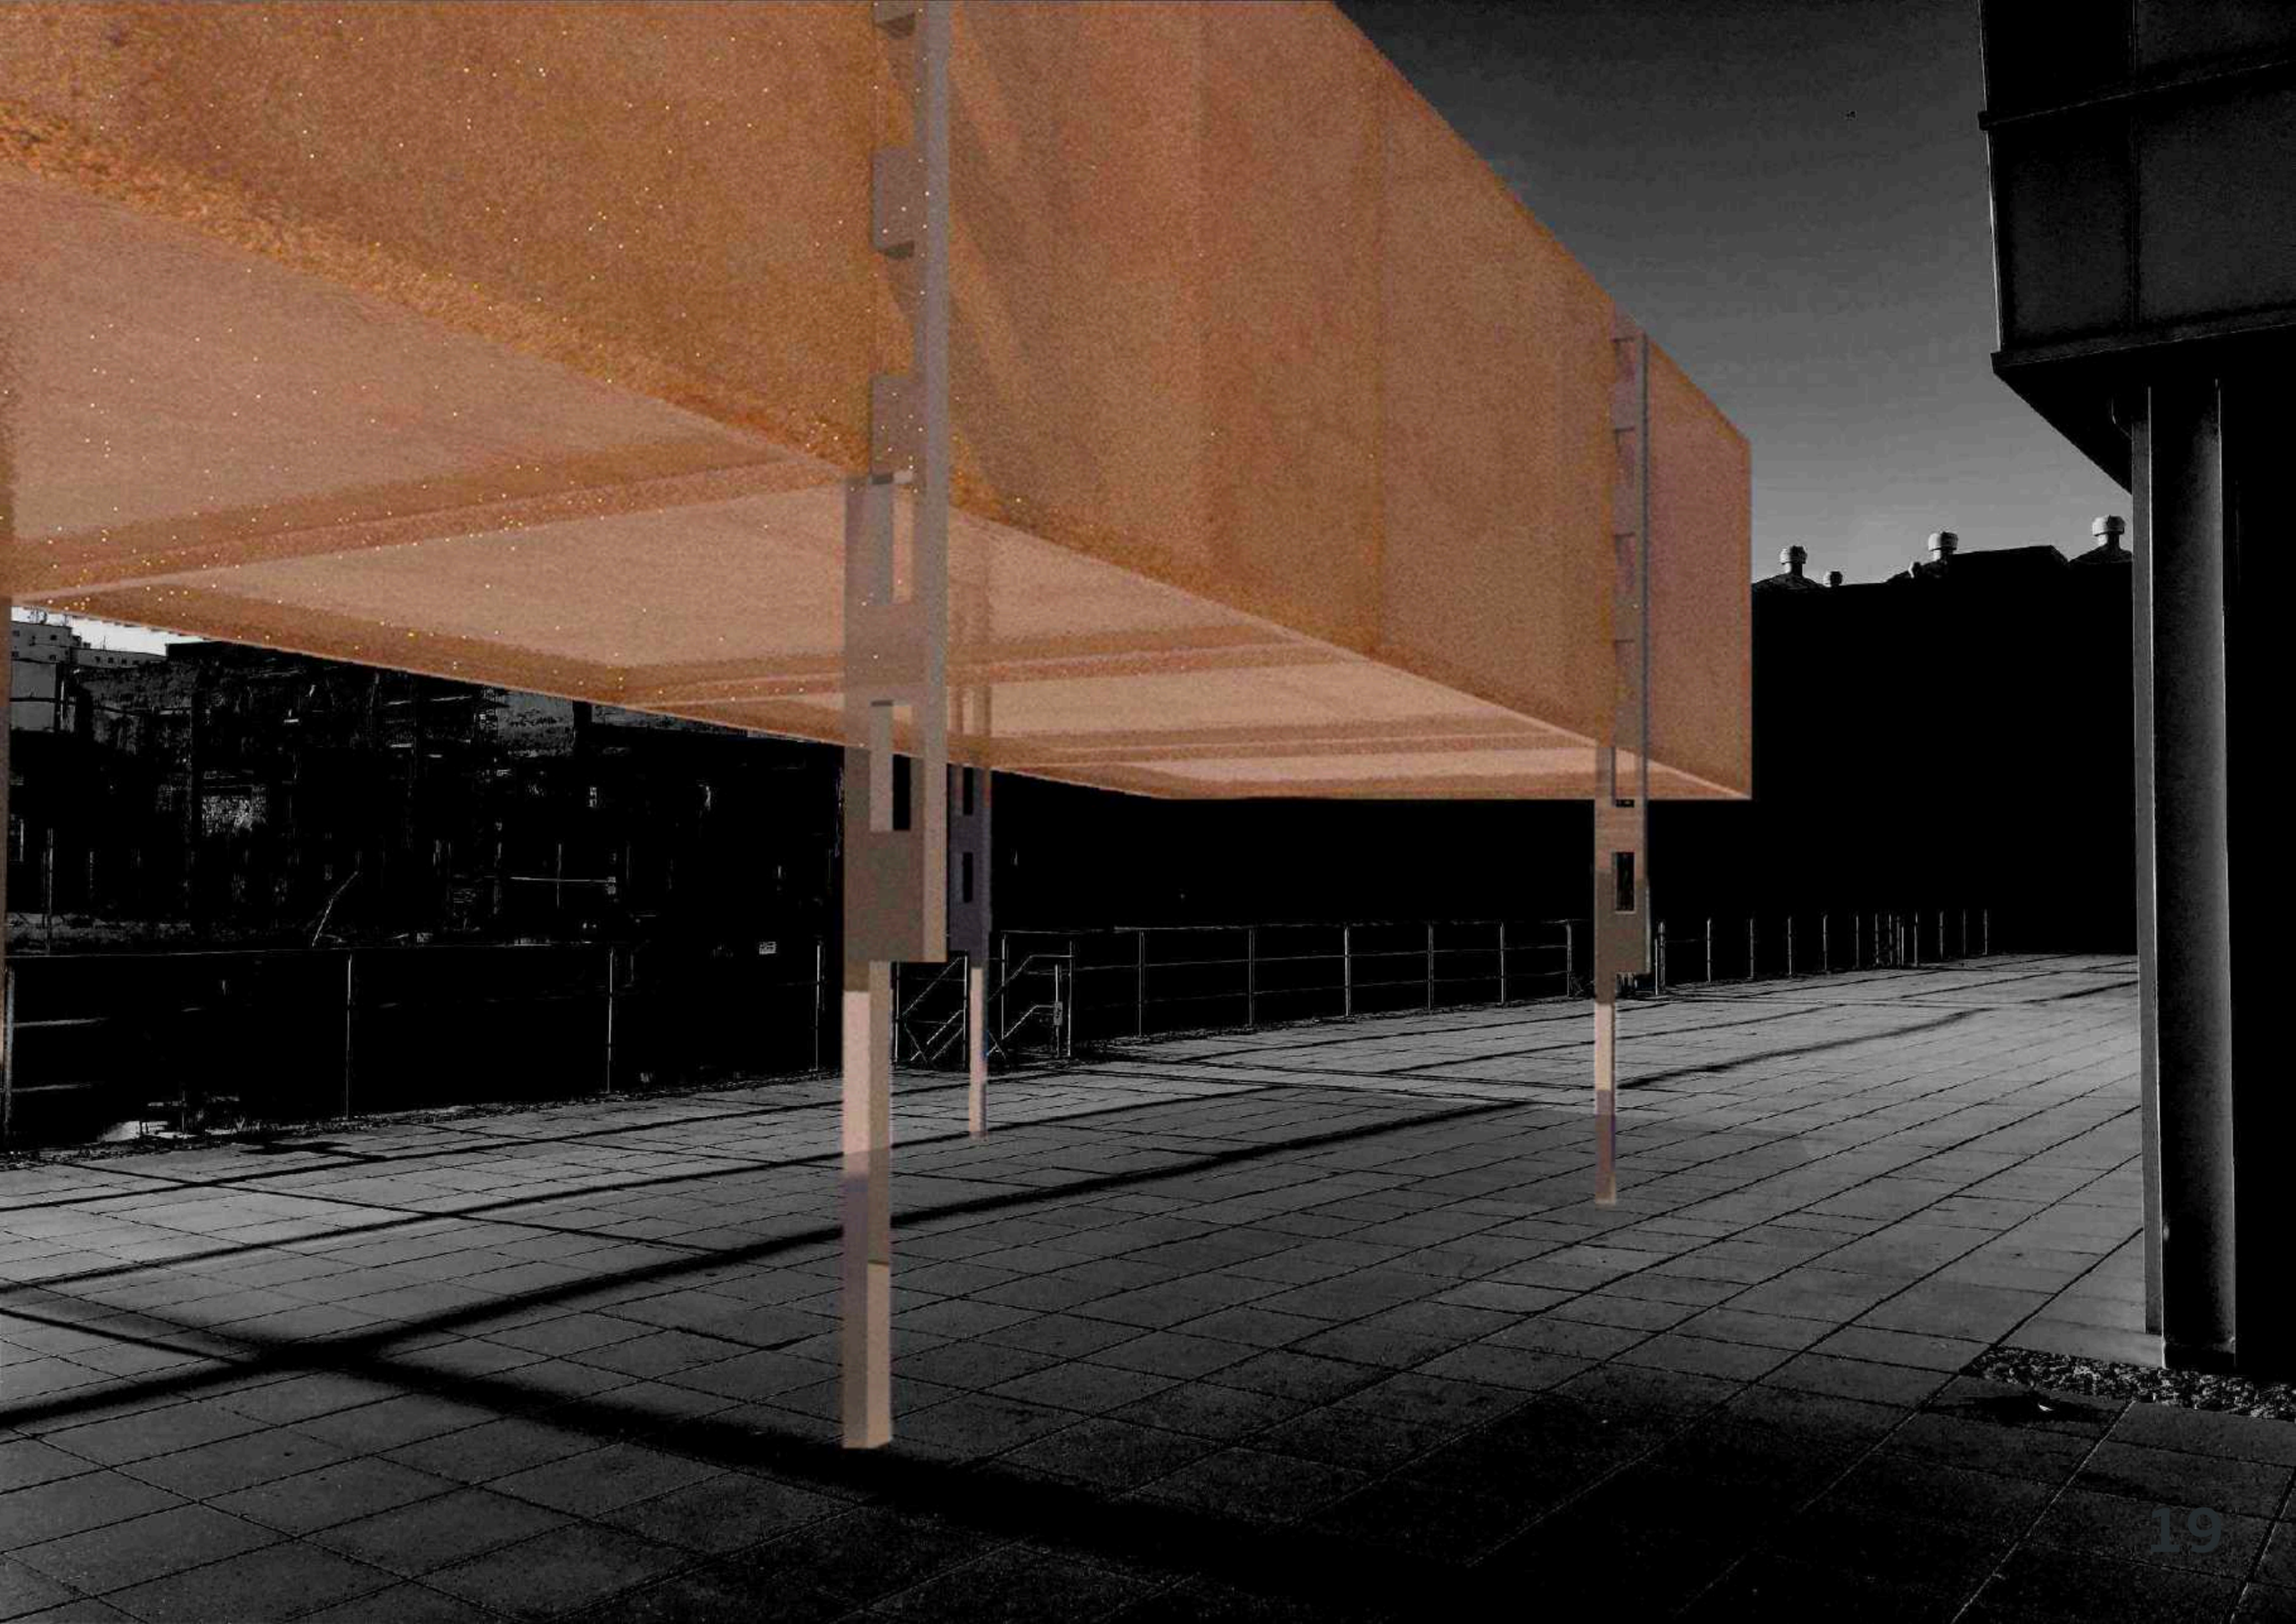




5 THE PRIVATE ONE



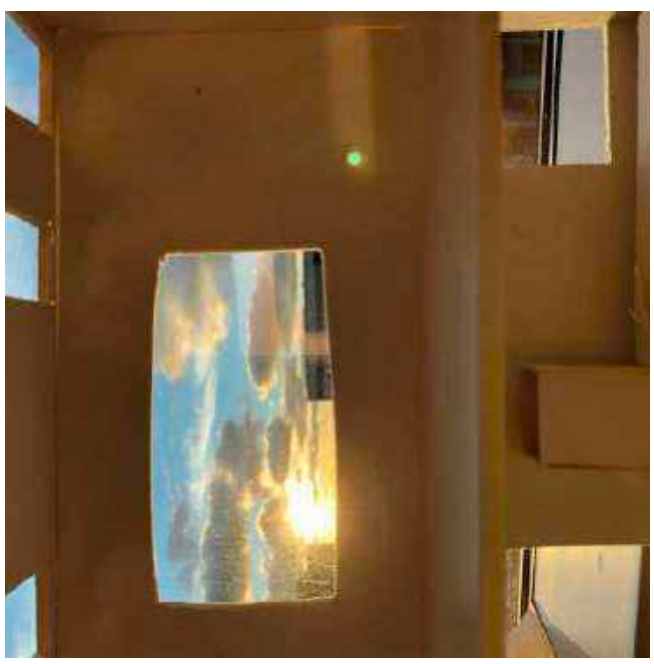





STUDENTLÄGENHET

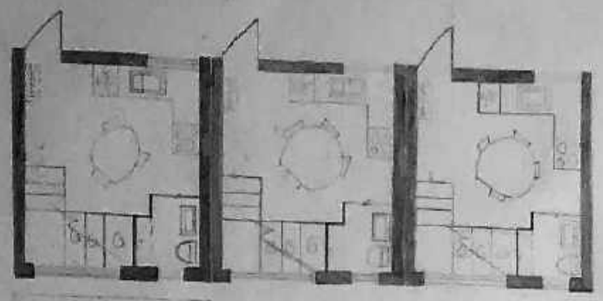


FLOOR PLAN 1
SCAL 1:50

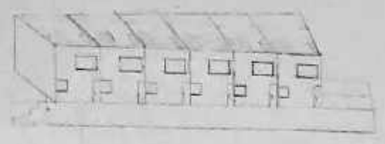


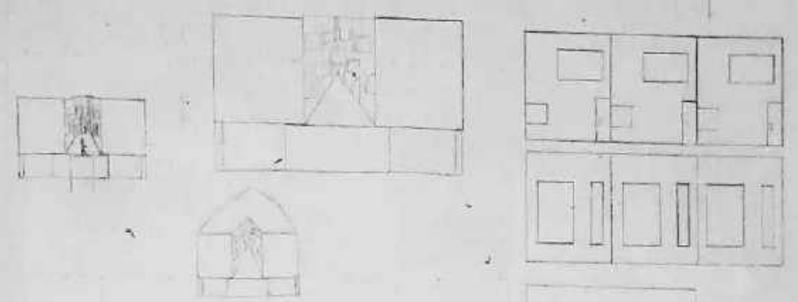

SCAL 1:100

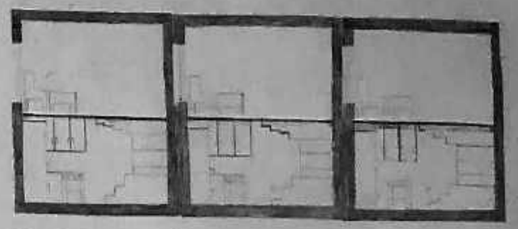


SITE SECTION A
SCAL 1:50

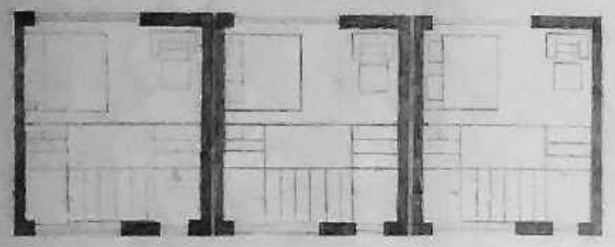


FLOOR PLAN 2
SCAL 1:50


THE PRIVATE ONE

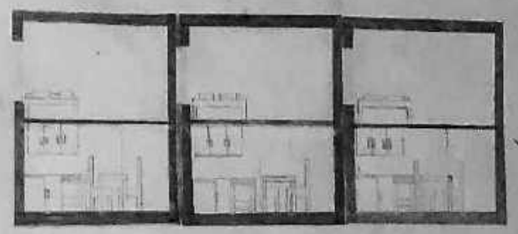

SITE SECTION B
SCAL 1:50

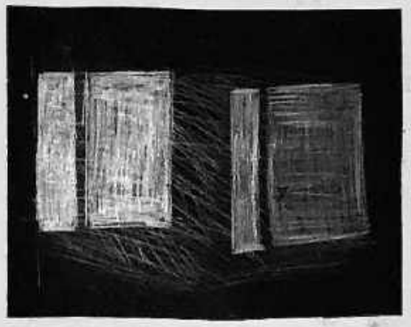


DOOR
SCAL 1:50

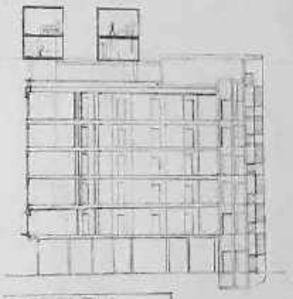


SITE SECTION
SCAL 1:200



PHOTO INSIDE

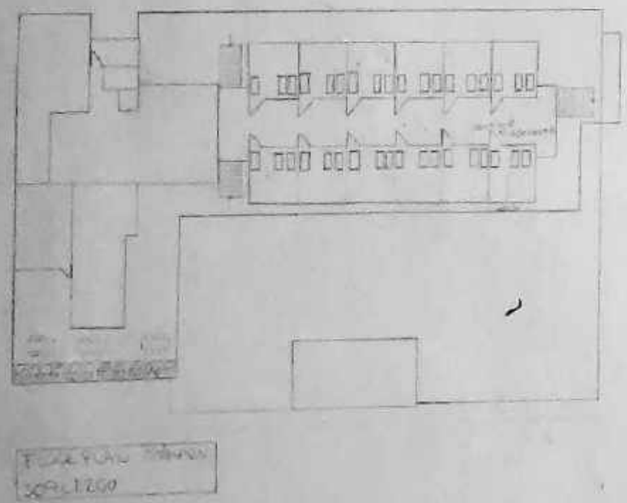

FLOOR PLAN PARKING
SCAL 1:200

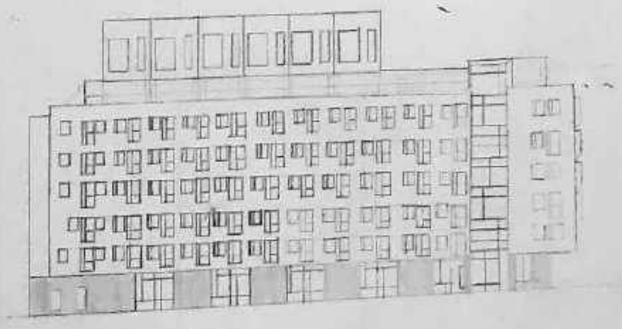

SCAL 1:200



6 Sege Park


ANEXITY

- KARTLÄGGNING AV SEGE PARK
MED HJÄLP AV FOTGRAFERING.
JAG VLADE ATT KLARLÄGGA
VENTILATIONER PÅ BYGGNADEN.
JAG SKPADE EN ARTIST BOOK,
MED NAMNET ANXIETY.
JAG VALDET ATT GÖRA
BILDERNA SVART OCH VITA.
SATTE IHOP ALLA BILDER FÖR
ATT SKAPA KÄNSLAN SOM
PLATSEN GAV MIG OCH EN
LÅDA.




HISS

ANXIETY

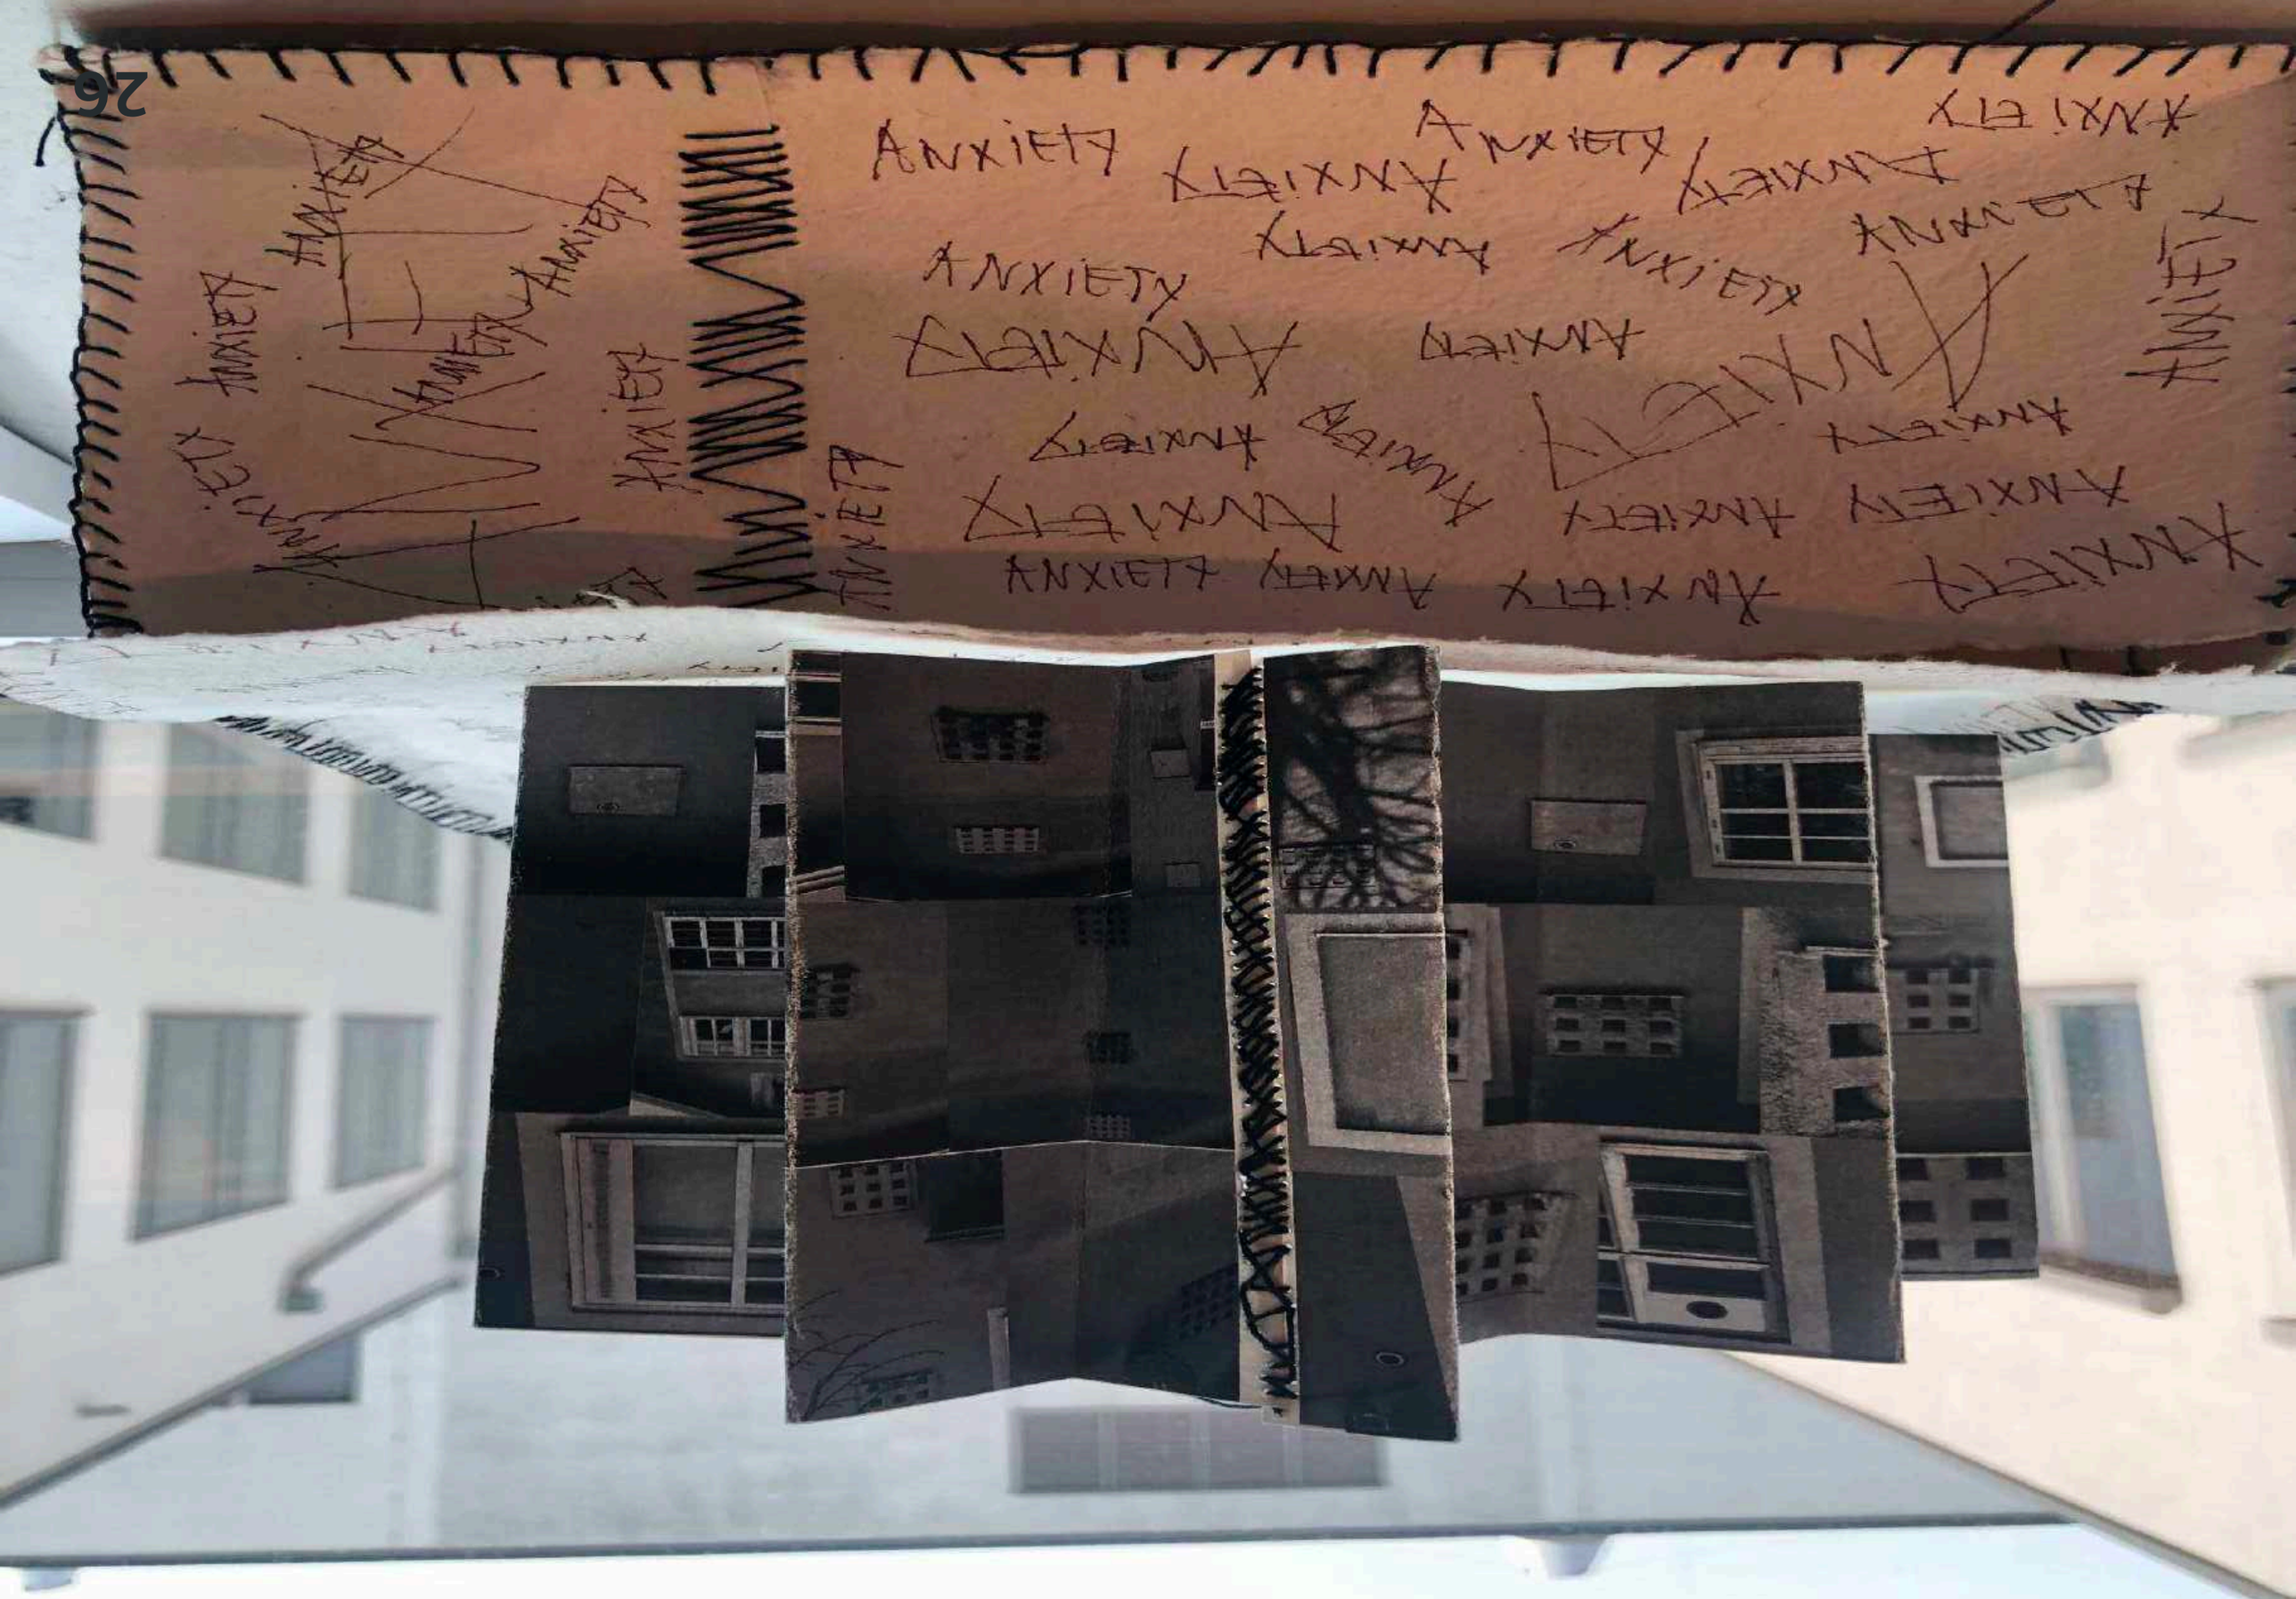



7 SÖDRA VERKET

Visualiseringar





- Projektet innebär att göra en omgestaltning av Södra verket i Lund. En process som började med att vi skapade en programhandling i grupp. Arbetet fortsatte enskilt och möjligheten att använda andra klasskamraters progamhandling.


ritningar i olika skalor, ex 1:200,1:400, 1:500 1:1000 1:100.

. Projekten redovisades i poster format, 6 stycken A1:or.




ÖVERSIKTSSPLAN 1:1000


Sektioner

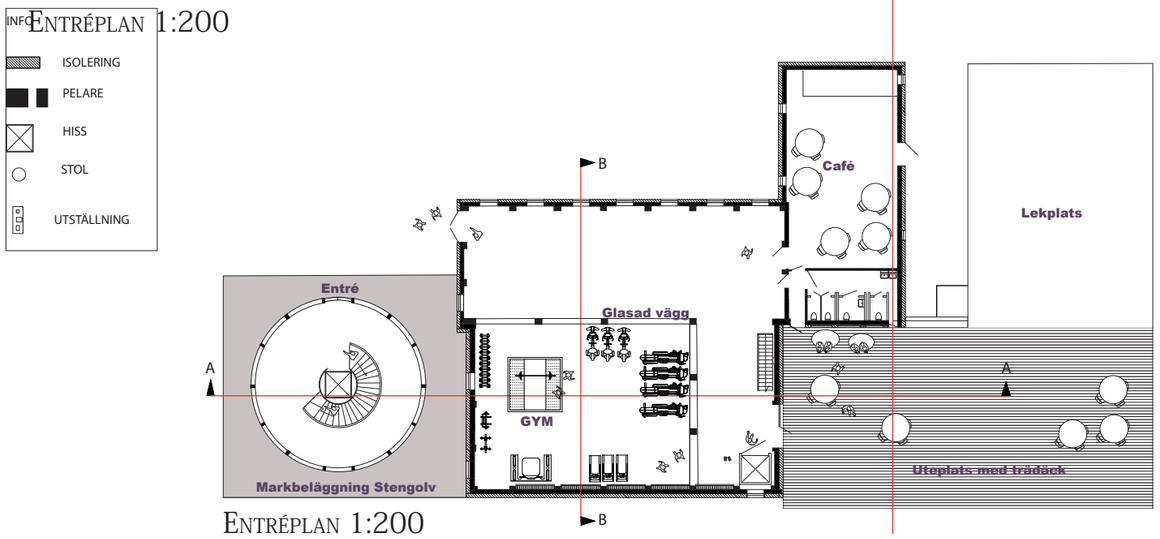


Entréplan 1:200

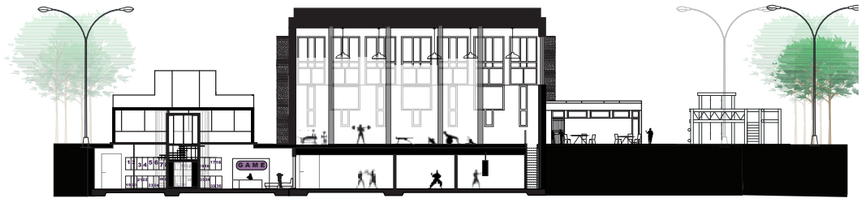


Sektion a-a 1:200

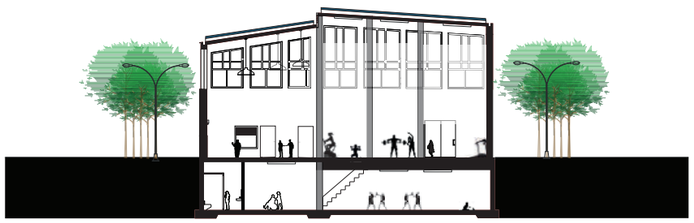

Sektion b-b 1:200

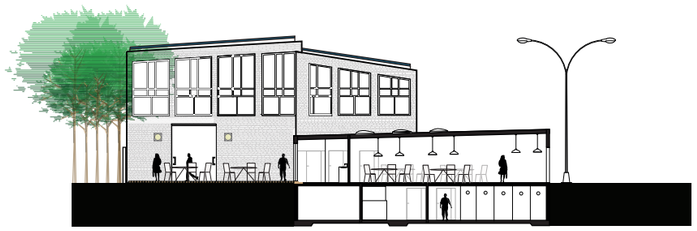

Sektion c-c 1:200

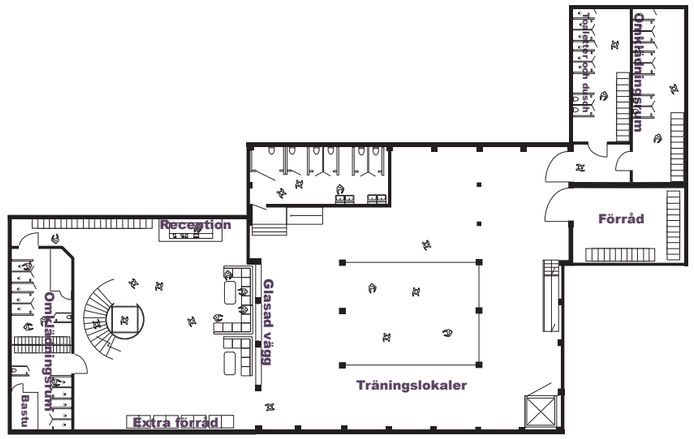

Källarplan 1:200

- Entréplan, Källarplan och sektioner för den nya omgestaltningen av Södra verket. Valet av det nya namnet, Game Street Klostergården kommer från inspirtaion från Game Street Mekka i Köpenhamn.


GAME



